



PLAN TECHNIQUE M et MME AZAIS



LE DÉTAIL
FRANÇAIS
DEPUIS 1948

MOBALPA BIARRITZ
LISA DUCOS
lisa@mobalpa-biarritz.fr
05 59 41 09 95

PLAN TECHNIQUE DU 20/09/2025

2	Arrivée eau froide évier en attente à	60 cm du sol
3	Arrivée eau chaude évier en attente à	60 cm du sol
4	Evacuation évier en attente à	50 cm du sol Diamètre 40
5	Arrivée eau froide lave vaisselle /robinet d'arrêt en attente à	50 cm du sol
6	Evacuation lave vaisselle et siphon en attente à	50 cm du sol
	Tenir compte de l'encombrement boîtier aqua stop LxHxP	80x90x40

ELECTRICITE		HAUTEUR COTES PRECONISEES
C	Alimentation plaque induction 32A	40 cm du sol
D	Prise four 20A	60 cm du sol
G	Prise lave vaisselle 20A et prévoir boîtier étanche	40 cm du sol
M	Prise crédence (choix final client)	sur 110 cm du sol
I	Prise réfrigérateur	40 cm du sol
F	Prise hotte	200 cm du sol
N	Sortie air vicié / Prévoir flexible alu de hotte diamètre 150 et grille d'évacuation en façade extérieure	en attente dans le caisson placo
O	Cable en attente pour alimentation prise ilot	40 cm du sol





**NI PRISE
NI TUYAUX
NI ROBINET
EN PARTIE BASSE**


SUIVANT CHOIX
CLIENT
L' M

ATTENTION : LES TRAVAUX DE PLOMBERIE ET D'ELECTRICITE SONT A LA CHARGE DU CLIENT

- l'appareillage impérativement mis en place avant pose mobilier
- plan technique préconisé par MOBALPA, le choix final reste au client
- plan technique doit être obligatoirement visé par client ou maître d'œuvre

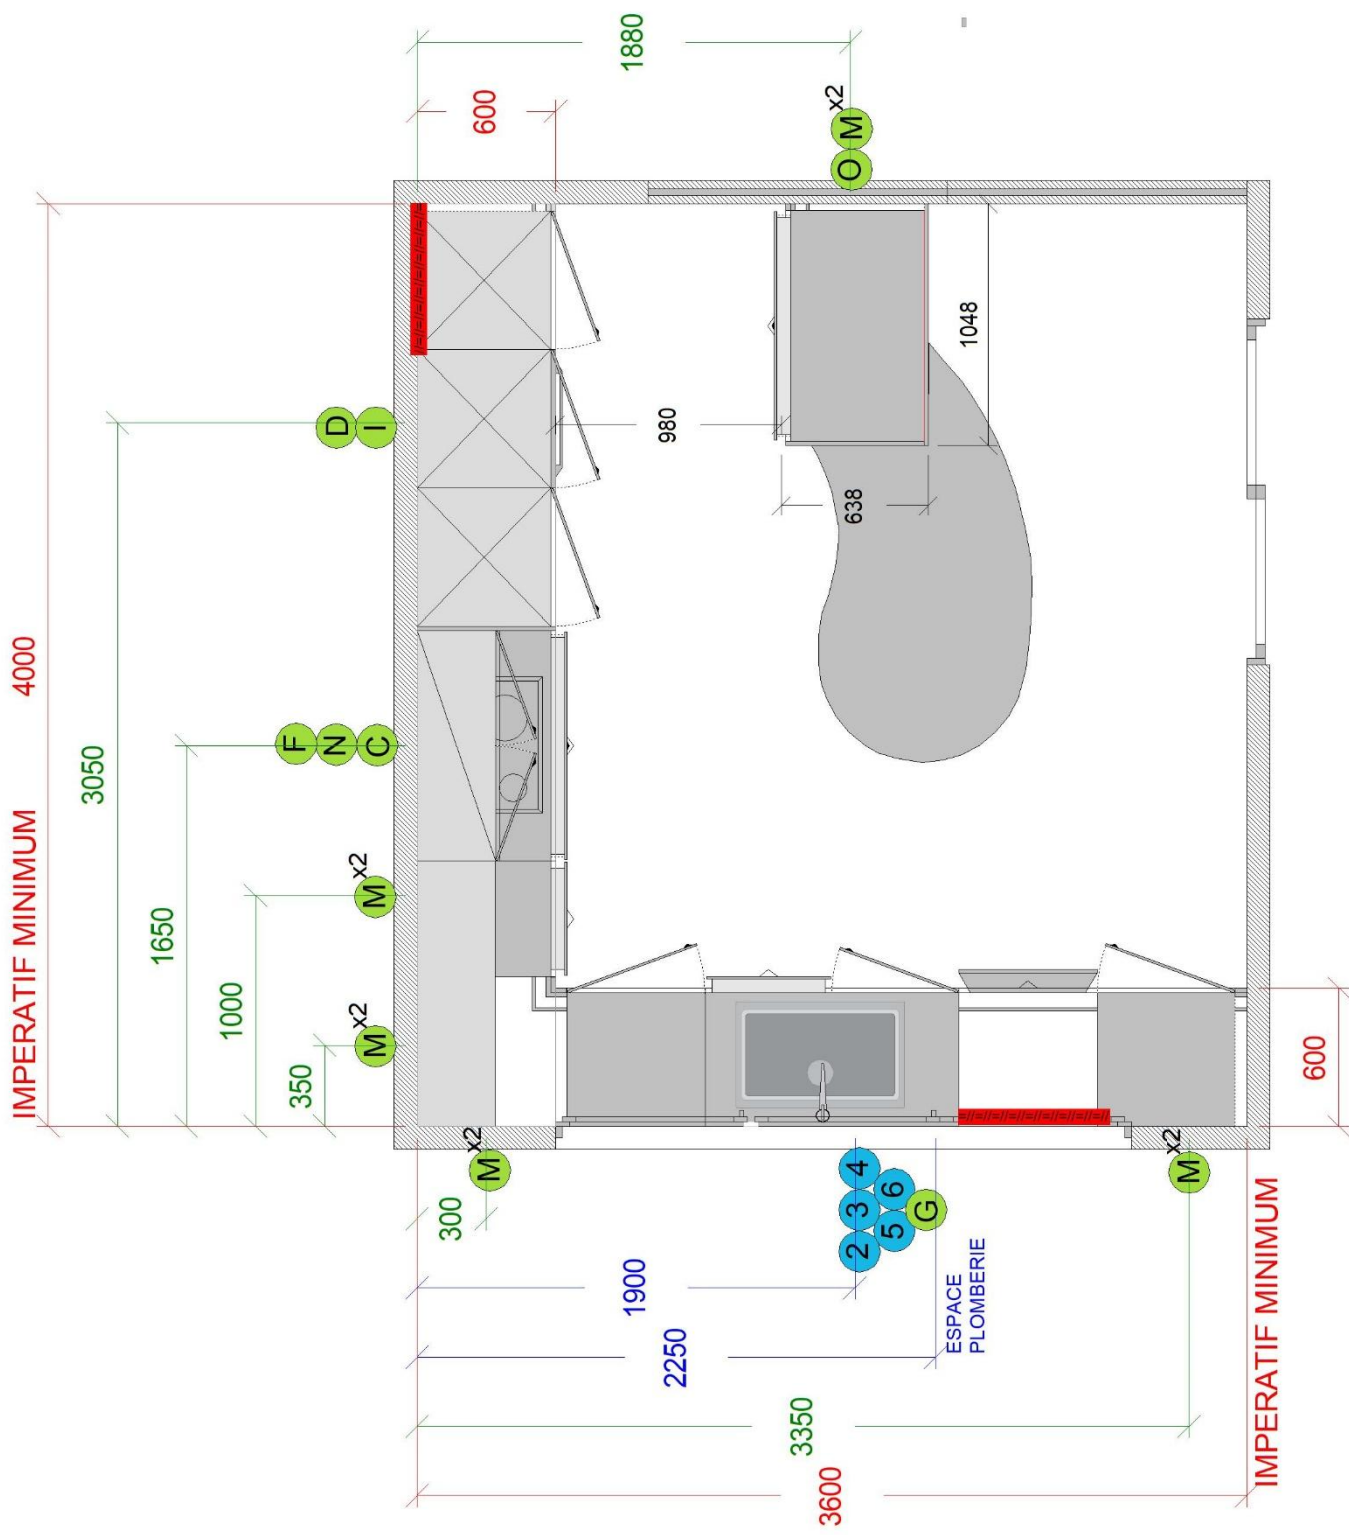

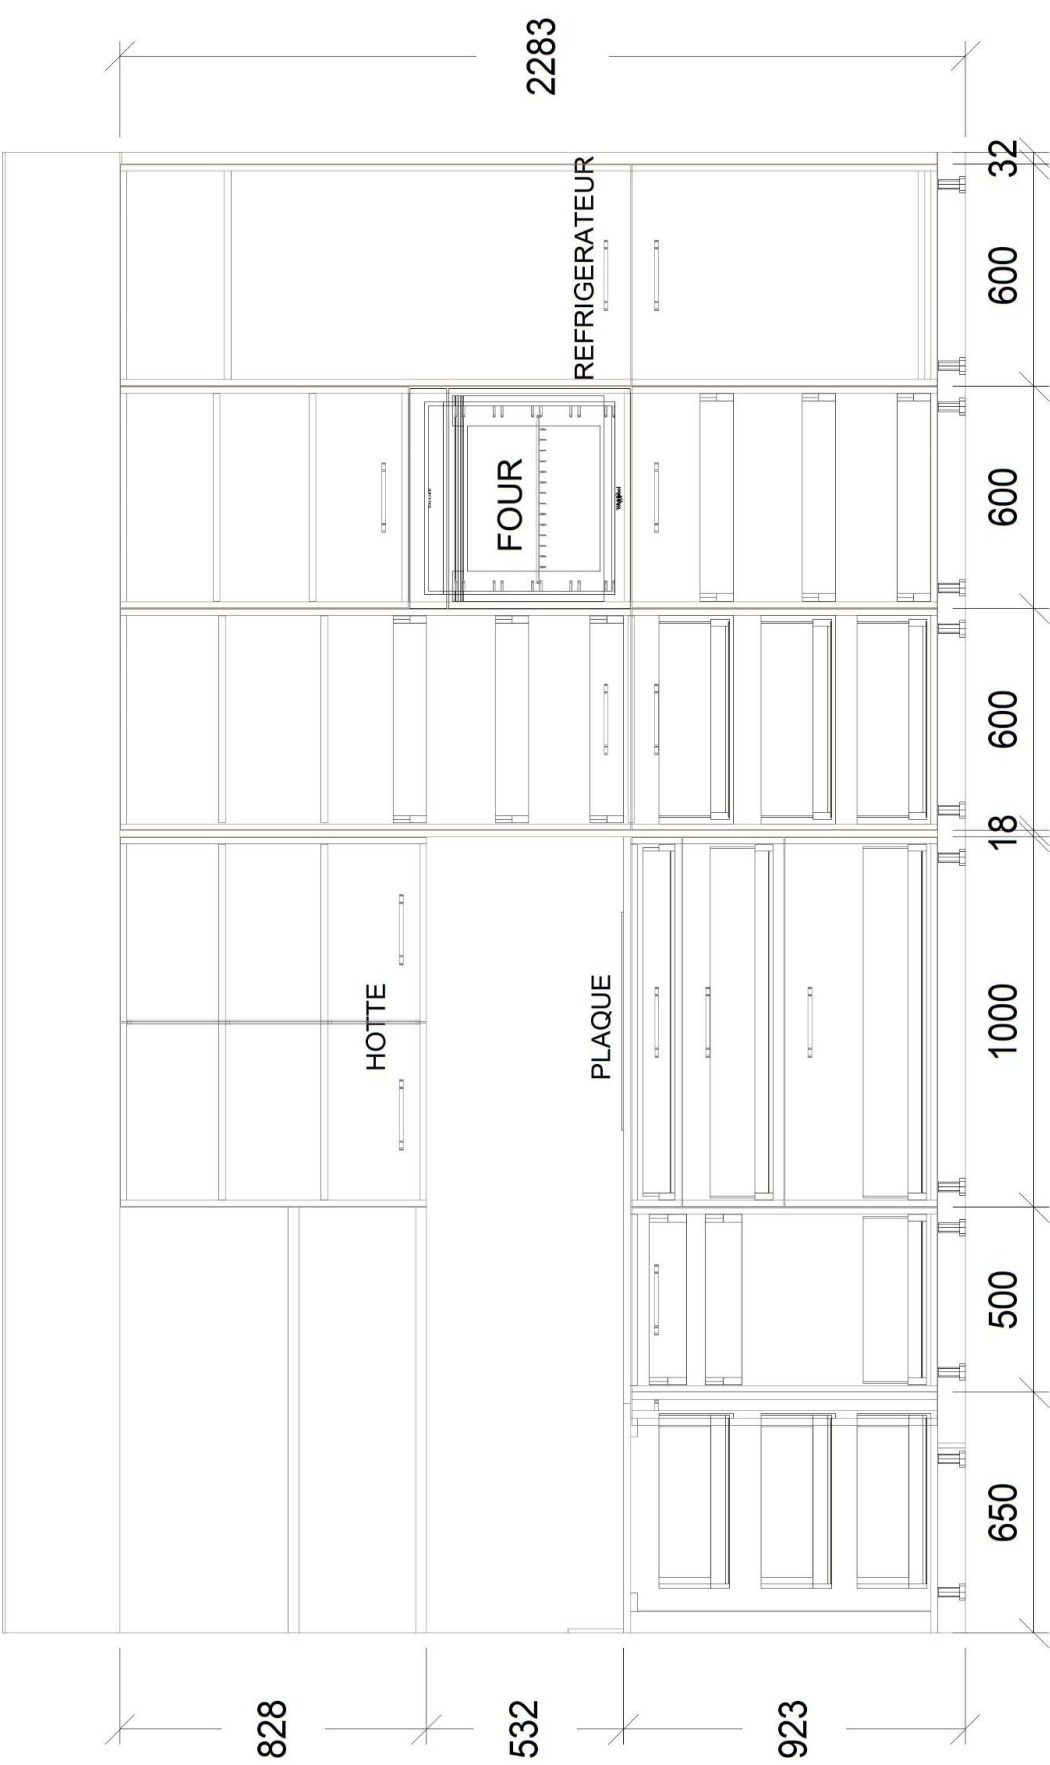

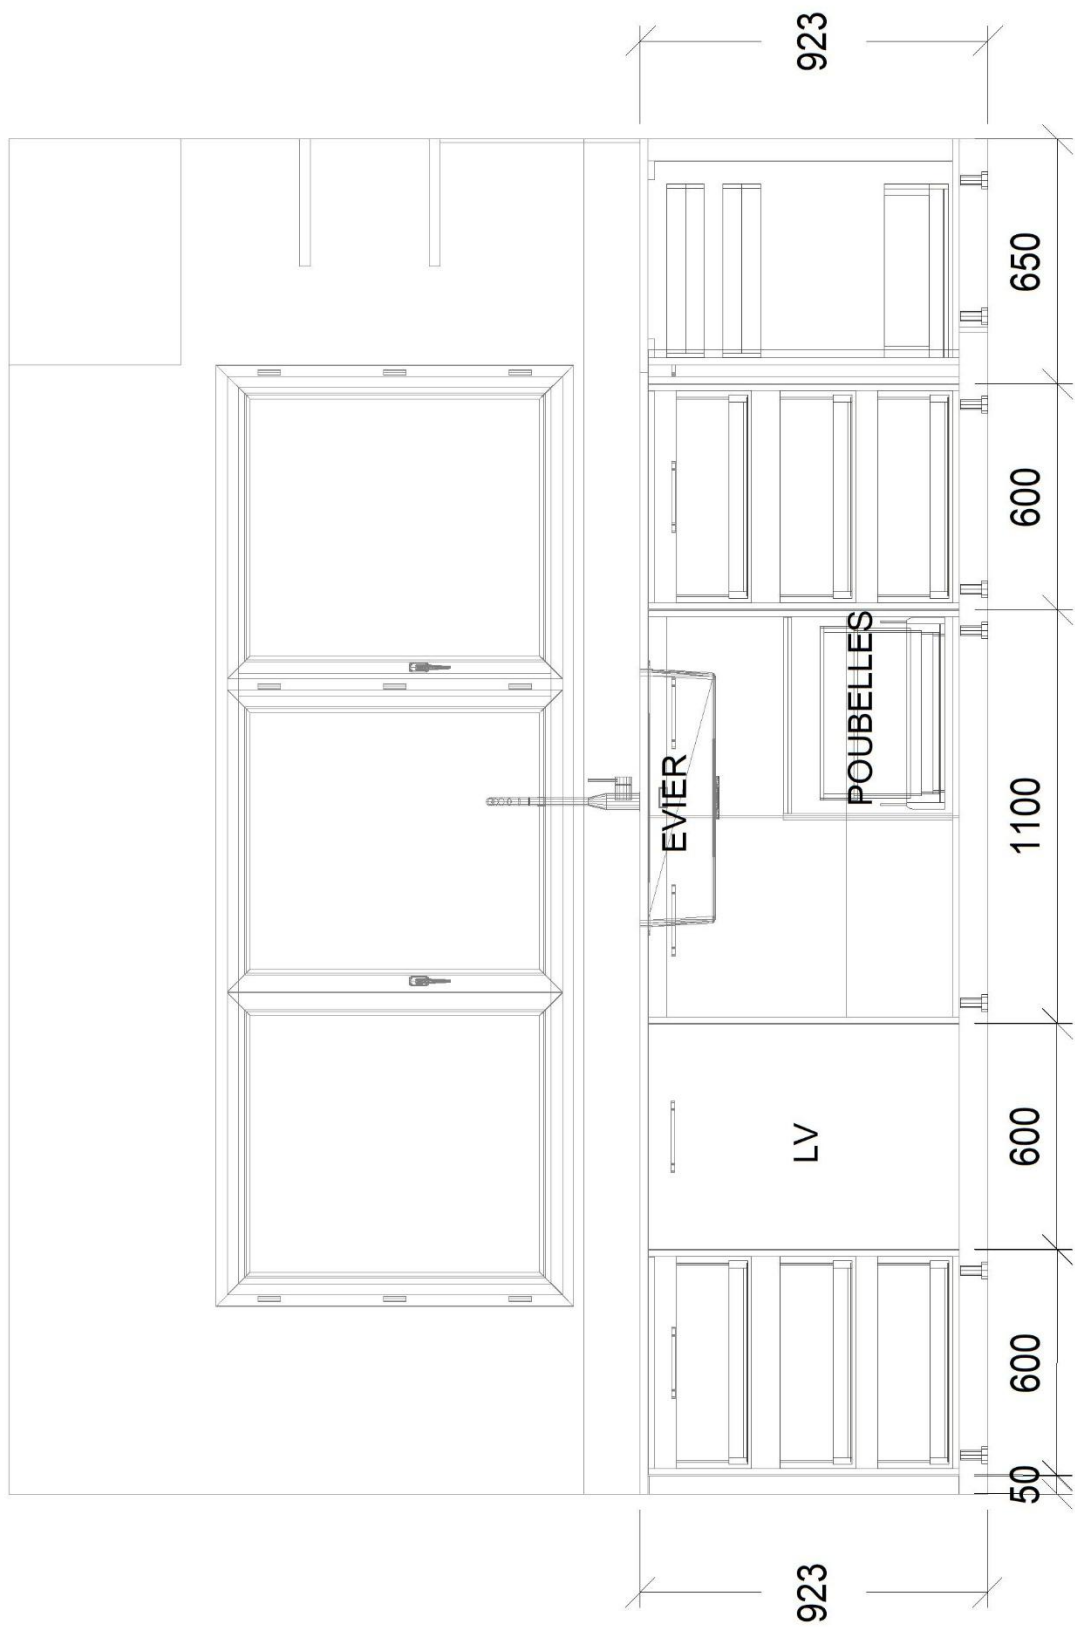

CAISSON PLACO A REALISER

